

Trunk Wadi Crossings

Ibri Sewer, TE Networks & STP — Concept Screening | Renardet 2621

0 5 10 km


 W2 Wadi crossings

W2 Trunk (concept)

 Main trunk (concept)

 Trunk branch (concept)

 W2 Streams

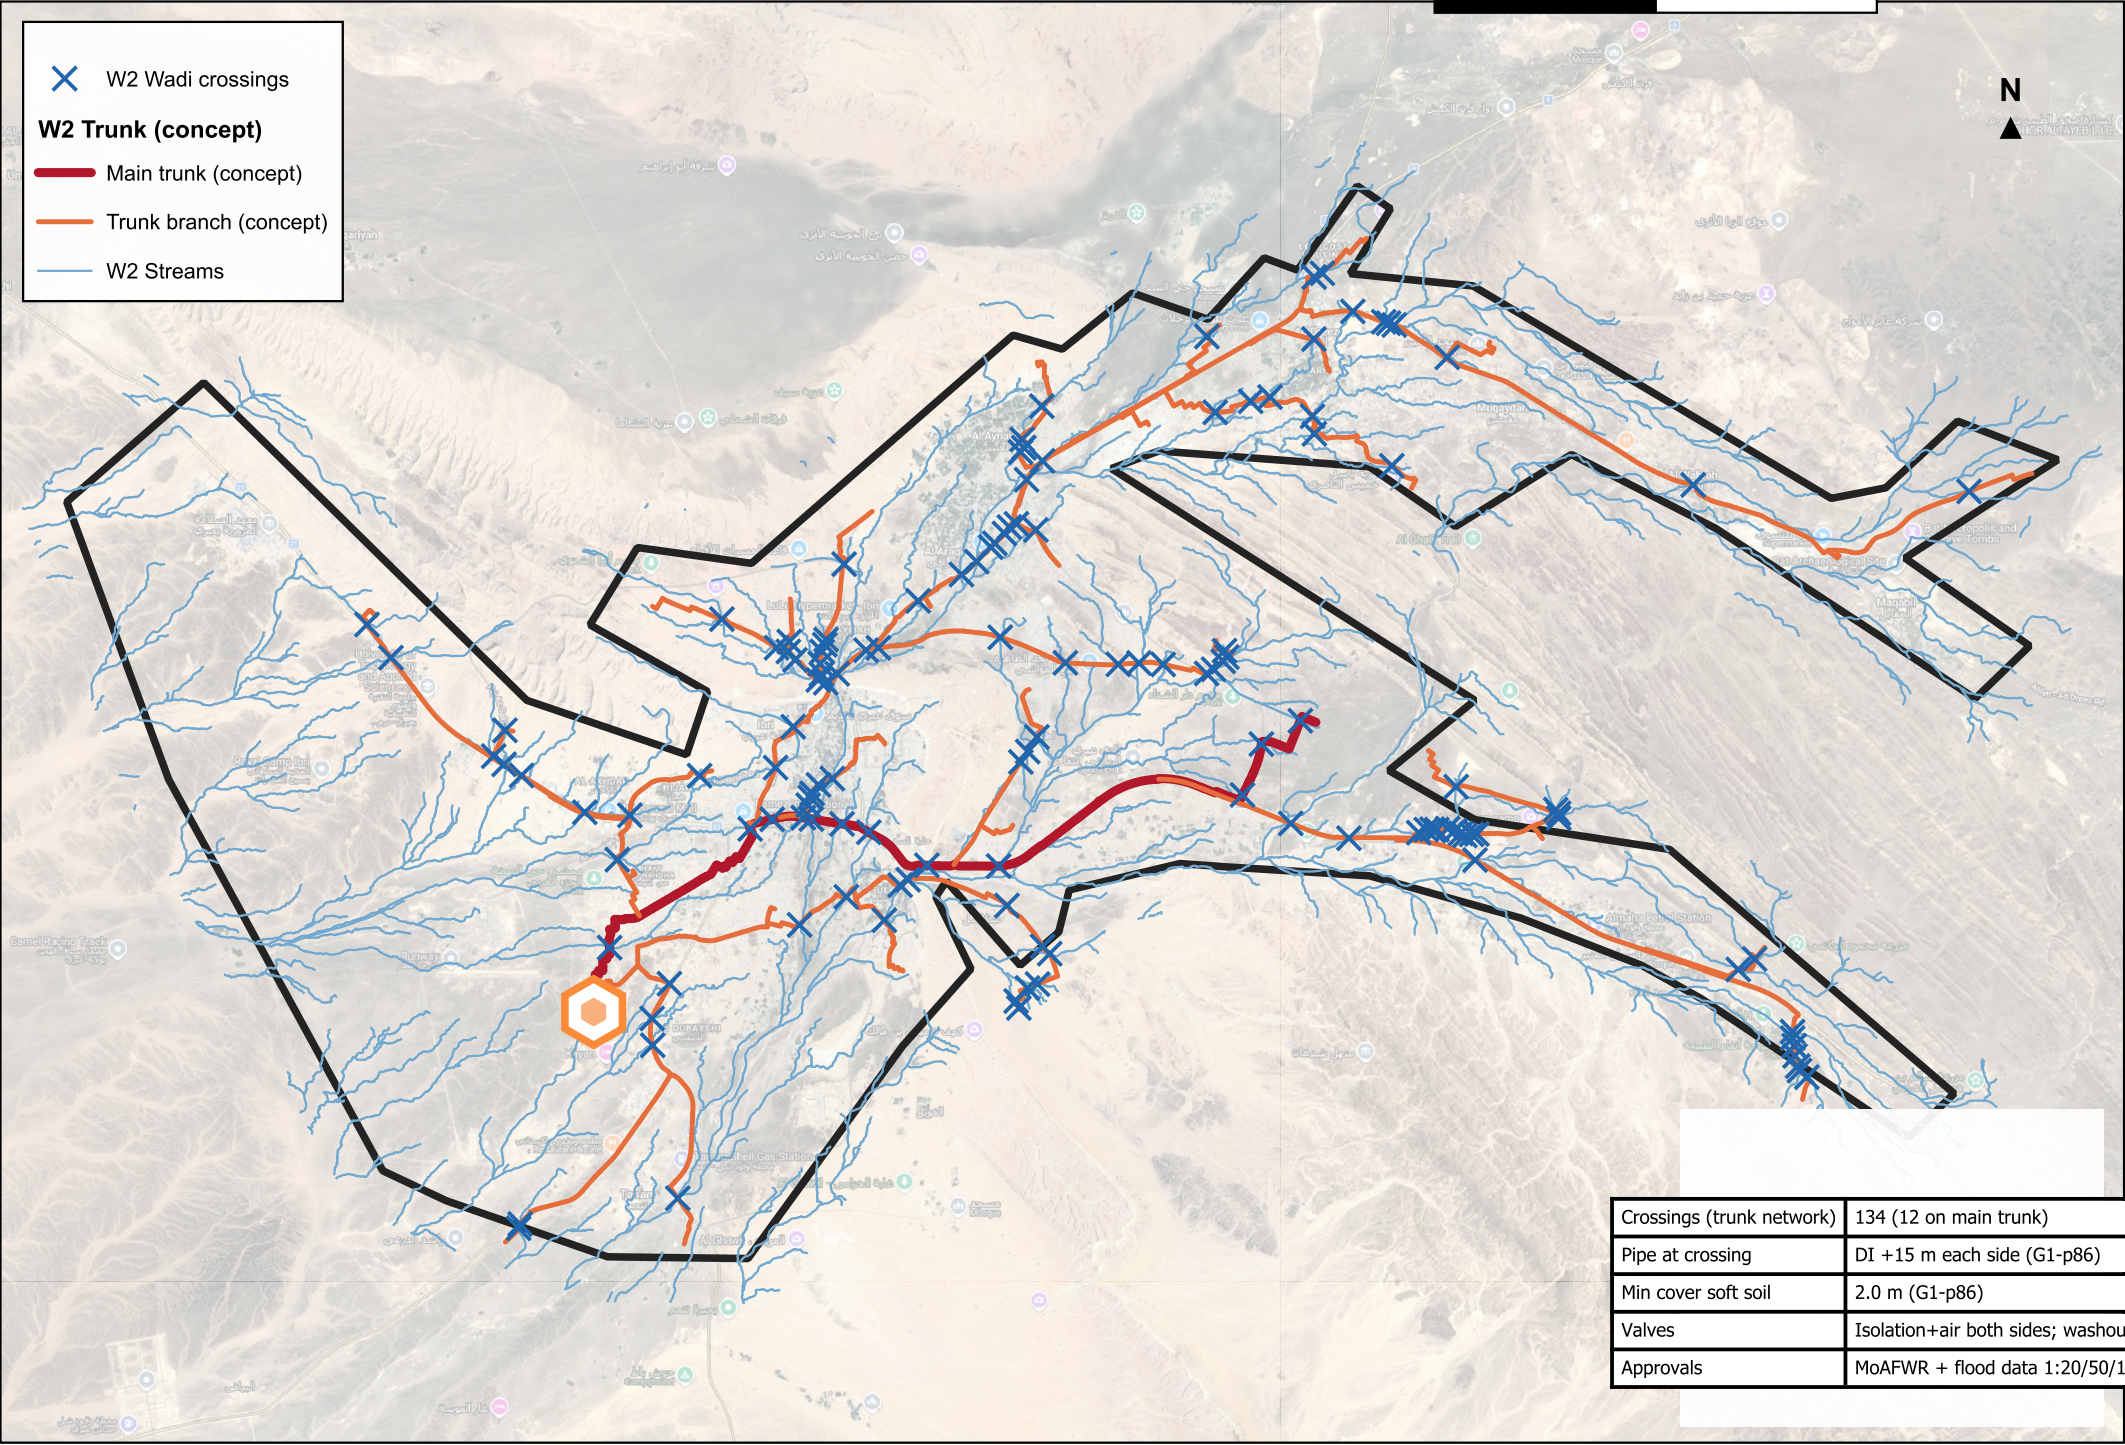

Crossings (trunk network)	134 (12 on main trunk)
Pipe at crossing	DI +15 m each side (G1-p86)
Min cover soft soil	2.0 m (G1-p86)
Valves	Isolation+air both sides; washout at low
Approvals	MoAFWR + flood data 1:20/50/100